
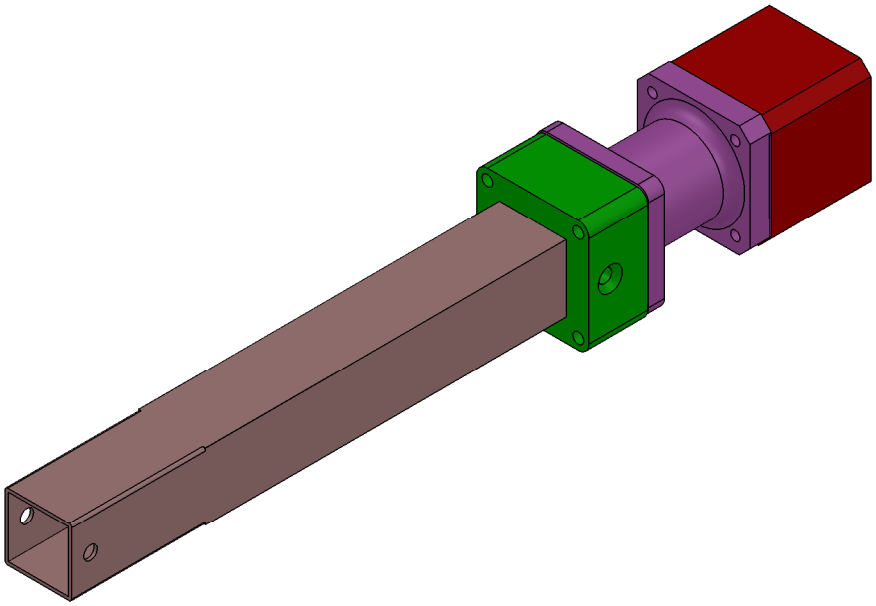


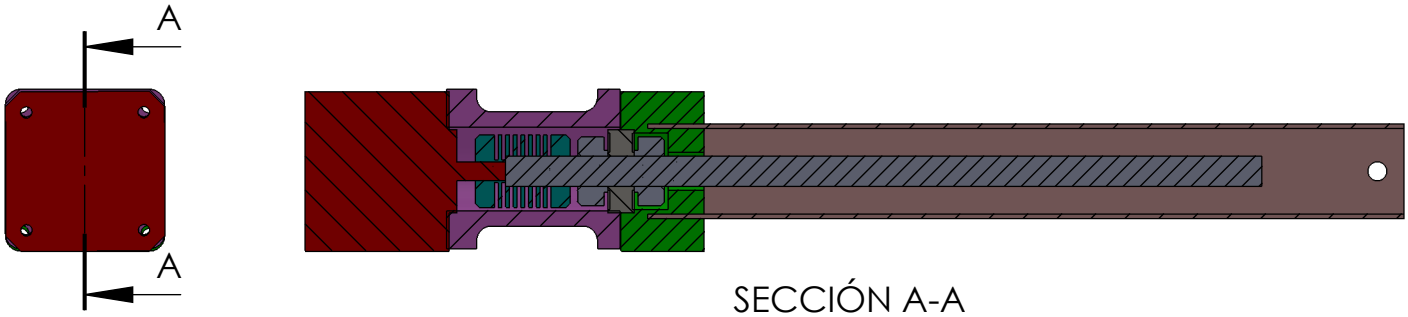

SECCIÓN A-A
ESCALA 1 : 2